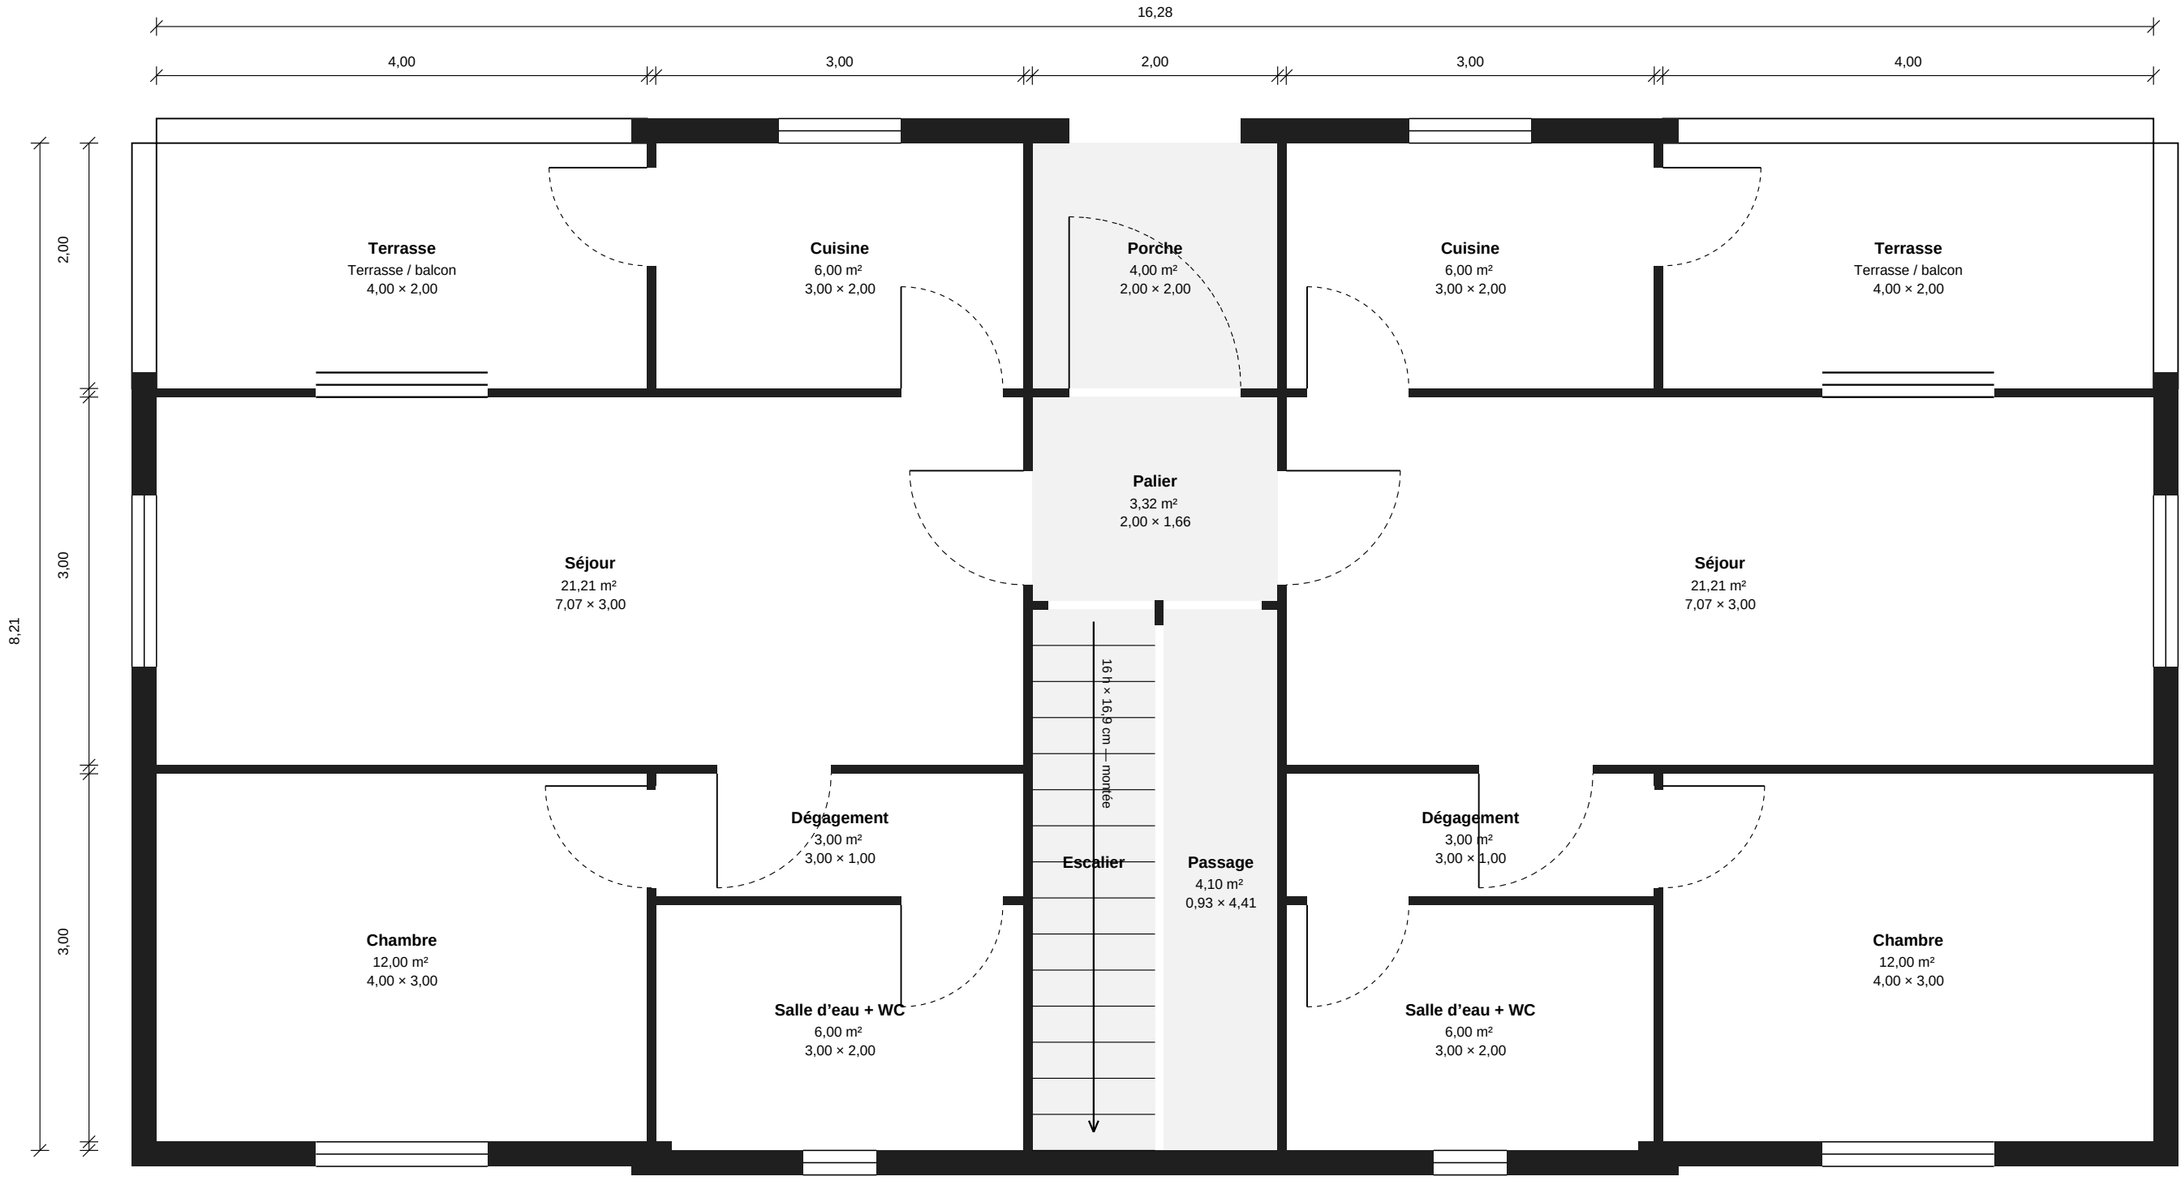


0 1 2 3 4 5 m

Surfaces habitables

RDC · Logement A	48,21 m²
RDC · Logement B	48,21 m²

Immeuble R+2 — 6 logements T2

Plan du RDC


Cotes intérieures en mètres. Surfaces calculées sur cotes intérieures.

Hauteur sous plafond 2,50 m — cloisons 7 cm — façades 20 cm.

Document d’étude non contractuel : à valider par un architecte et un bureau de contrôle.

Référentiel : textes français et ergonomie Neufert (référence de pratique).

Échelle	1/50
Format	A3
Date	19/10/2026
Indice	A — esquisse
Planche	1/3
Établi avec	Plan3D

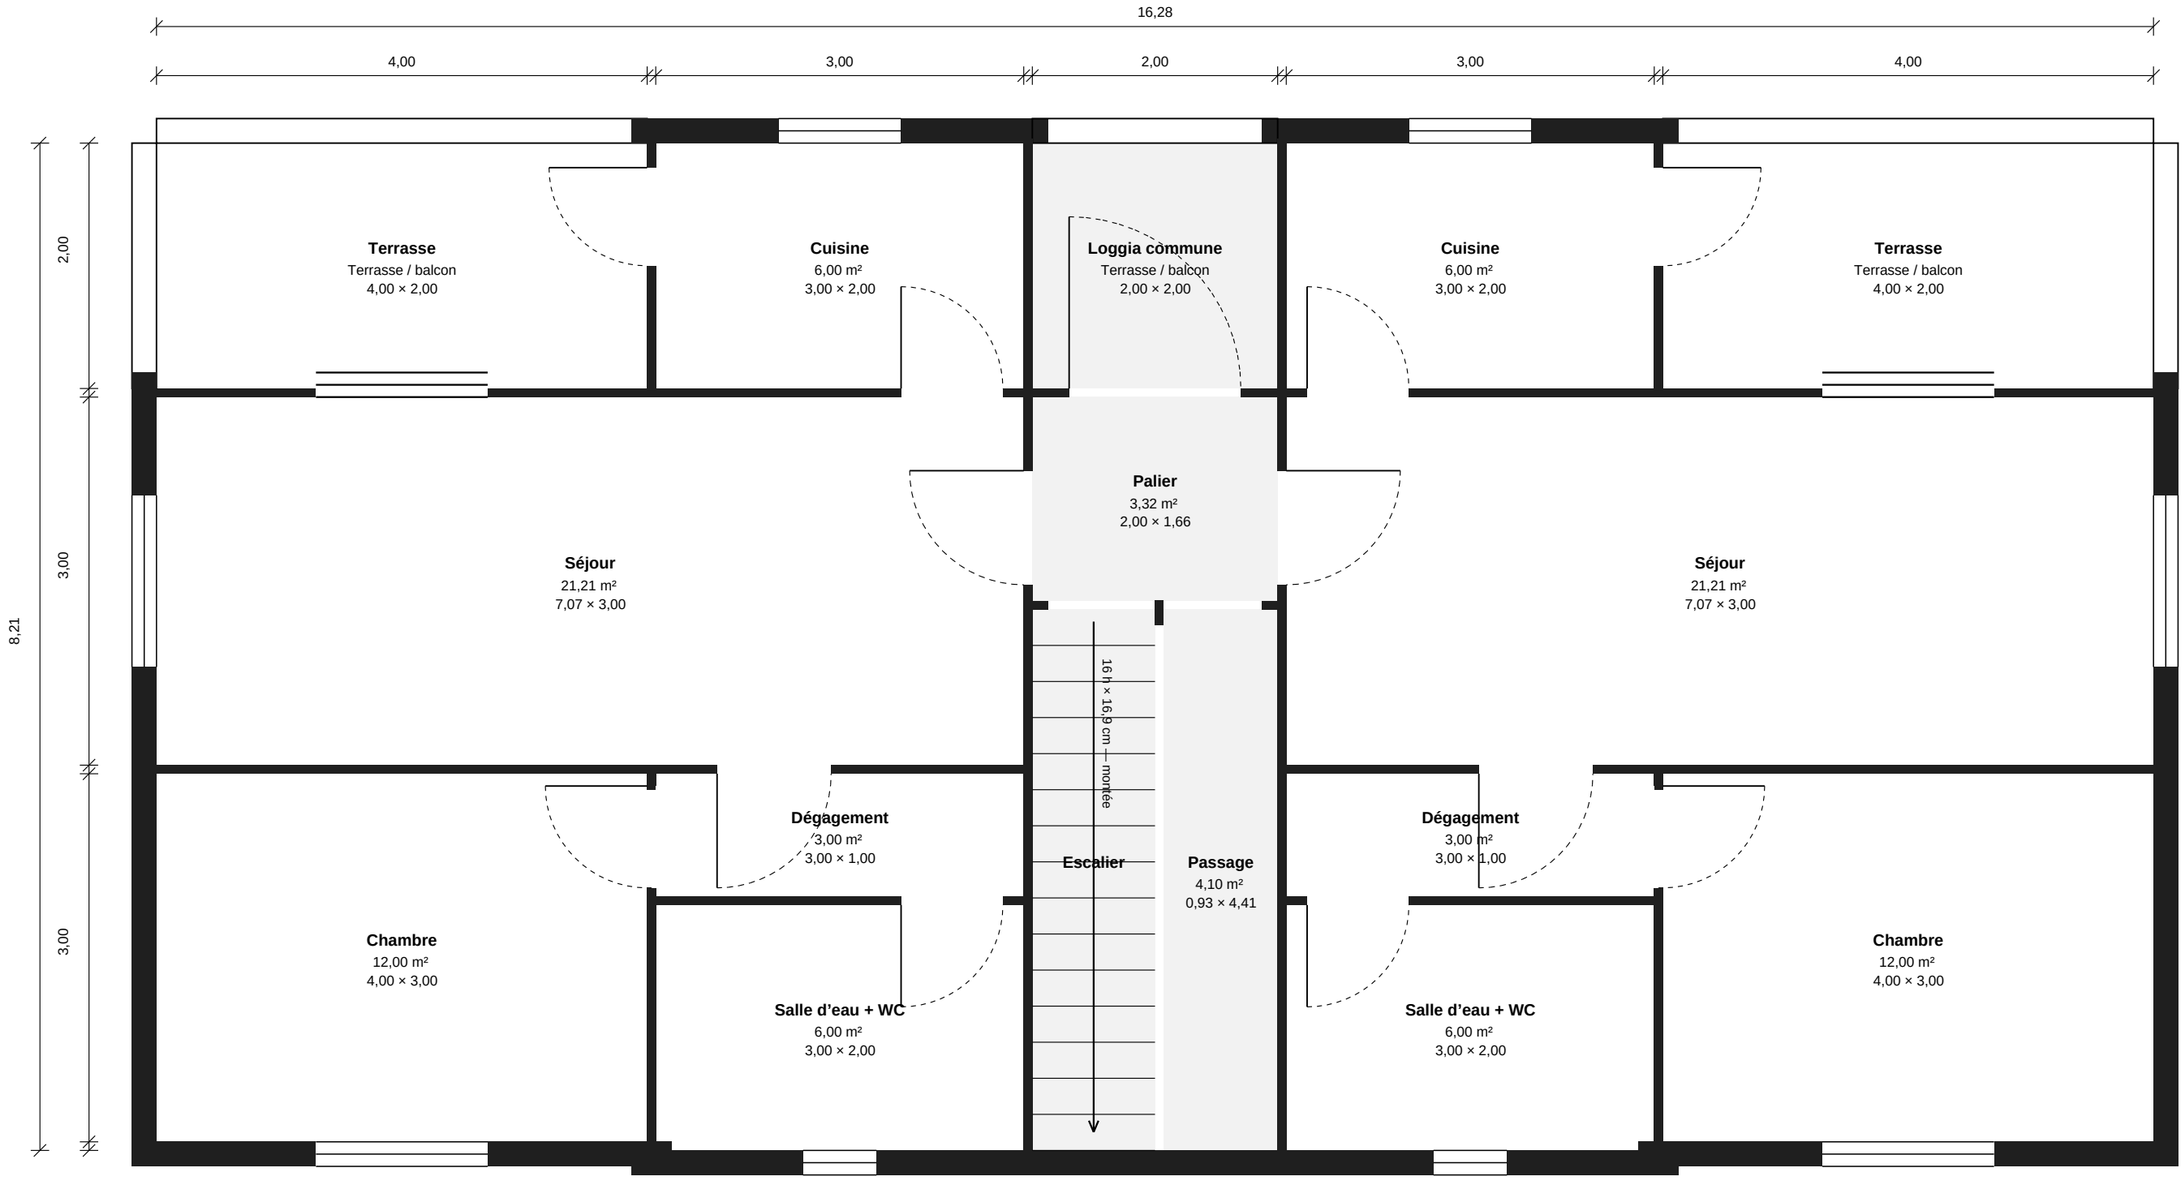

0 1 2 3 4 5 m

Surfaces habitables

R+1 · Logement A	48,21 m²
R+1 · Logement B	48,21 m²

Immeuble R+2 — 6 logements T2

Plan du R+1


Cotes intérieures en mètres. Surfaces calculées sur cotes intérieures.

Hauteur sous plafond 2,50 m — cloisons 7 cm — façades 20 cm.

Document d’étude non contractuel : à valider par un architecte et un bureau de contrôle.

Référentiel : textes français et ergonomie Neufert (référence de pratique).

Échelle	1/50
Format	A3
Date	19/10/2026
Indice	A — esquisse
Planche	2/3
Établi avec	Plan3D

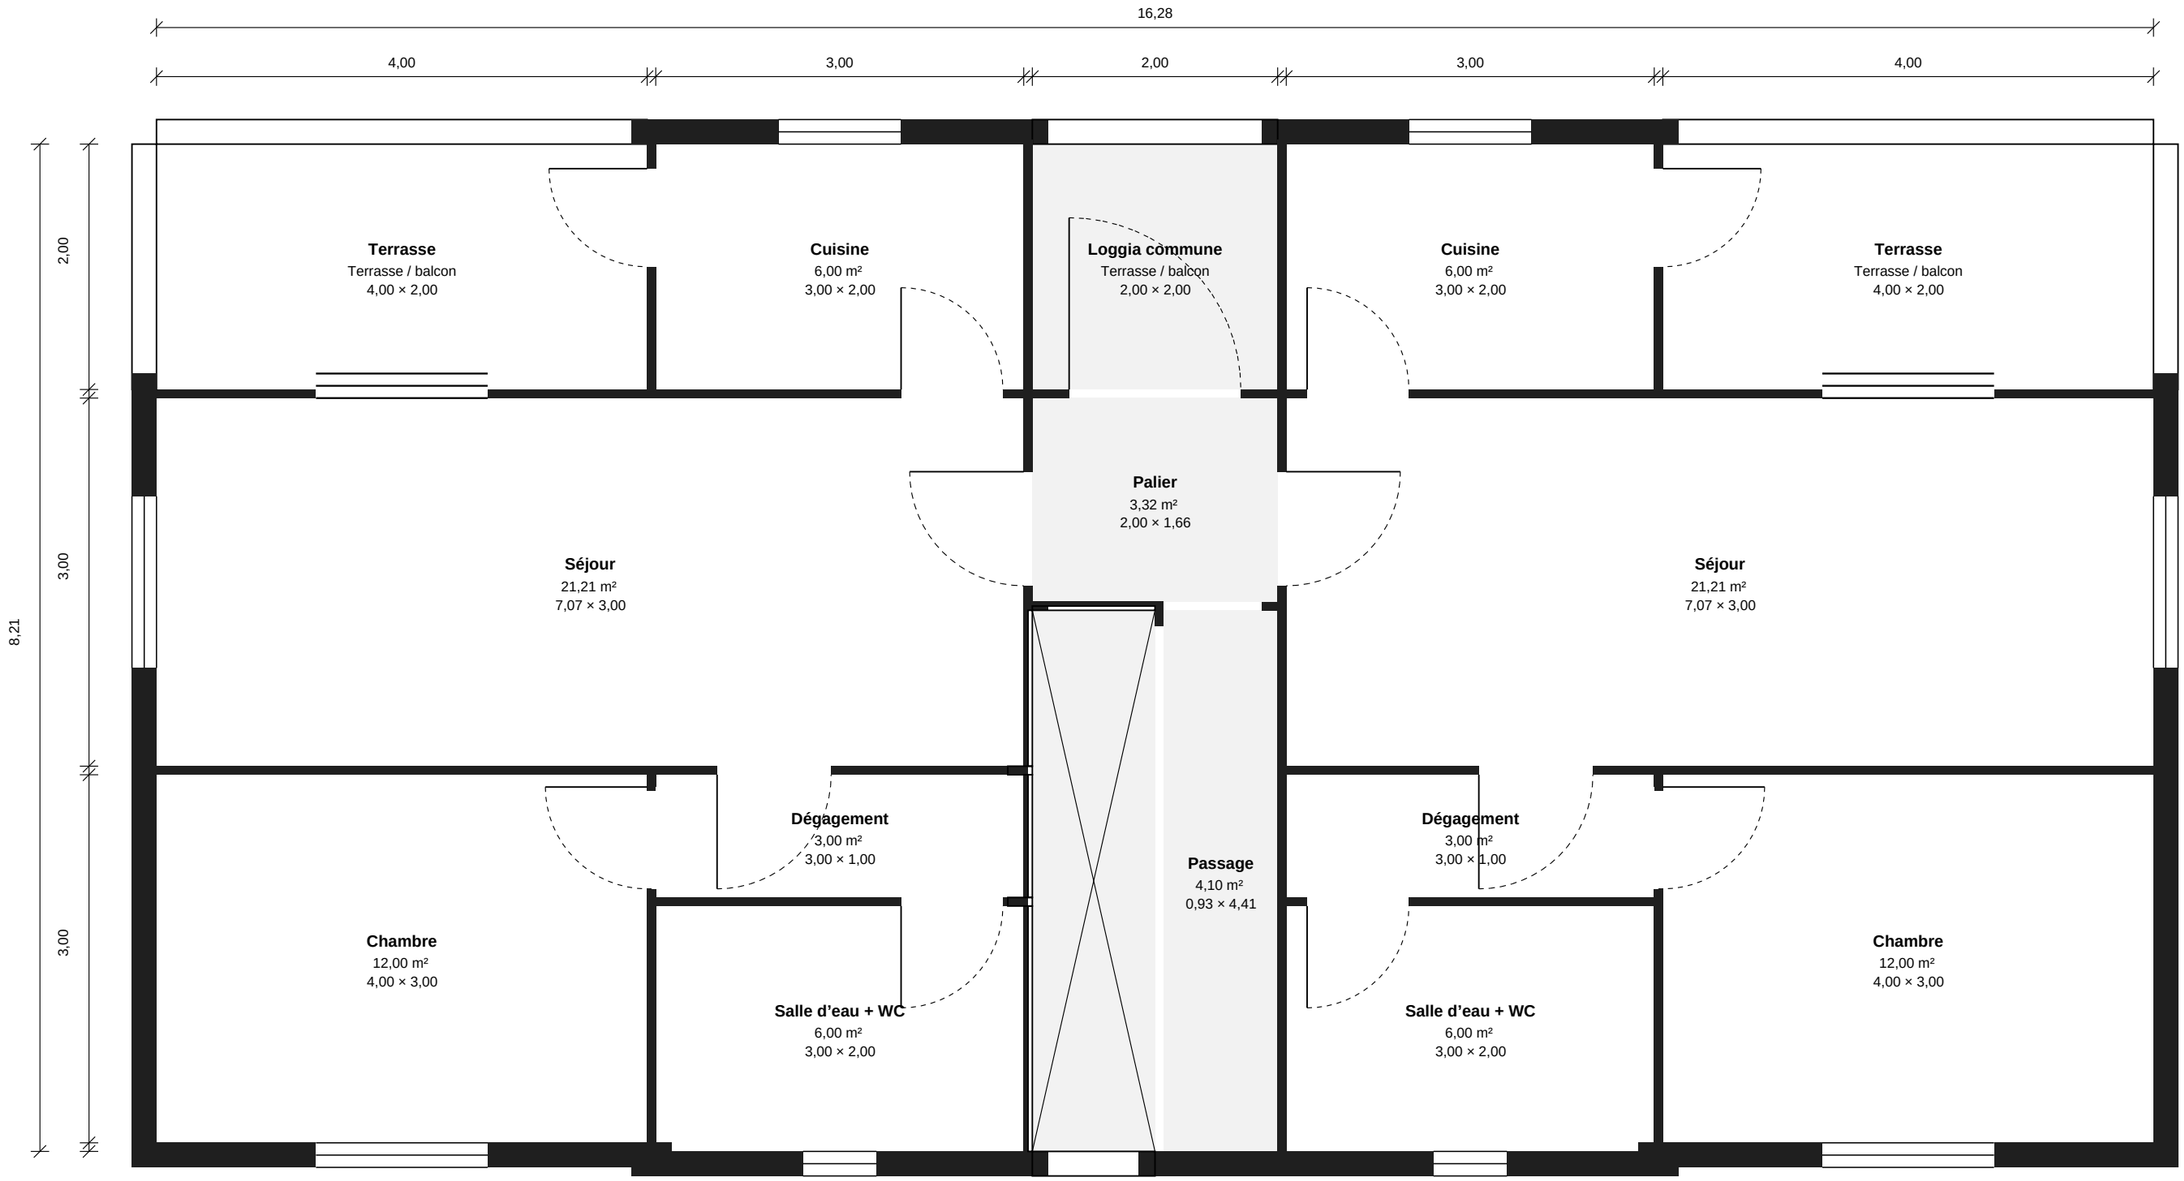

0 1 2 3 4 5 m

Surfaces habitables

R+2 · Logement A	48,21 m²
R+2 · Logement B	48,21 m²

Immeuble R+2 — 6 logements T2

Plan du R+2

Cotes intérieures en mètres. Surfaces calculées sur cotes intérieures.

Hauteur sous plafond 2,50 m — cloisons 7 cm — façades 20 cm.

Document d’étude non contractuel : à valider par un architecte et un bureau de contrôle.

Référentiel : textes français et ergonomie Neufert (référence de pratique).

Échelle	1/50
Format	A3
Date	19/10/2026
Indice	A — esquisse
Planche	3/3
Établi avec	Plan3D